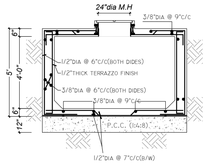
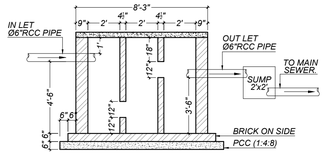


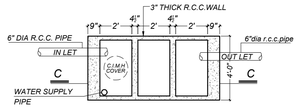

SECTION OF OVER HEAD WATER TANK
SCALE : 1"=4'-0"



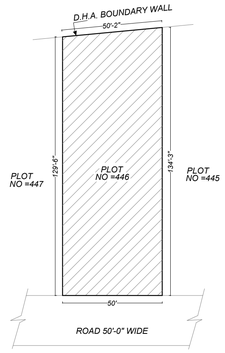

UNDER GROUND WATER TANK
SCALE : 1"=4'-0"



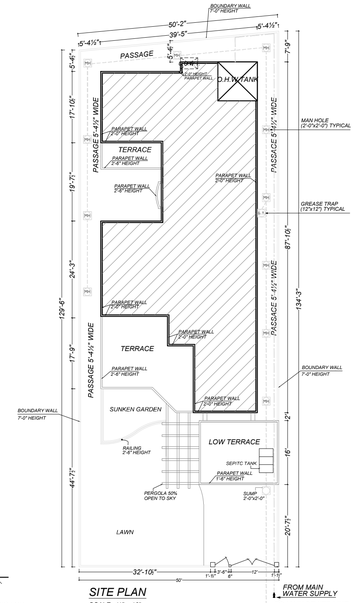

SECTION AT C-C
SCALE 1"=4'-0"



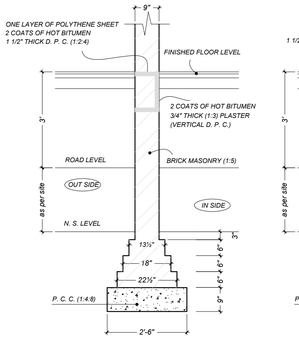

SEPTIC TANK PLAN
SCALE : 1"=4'-0"



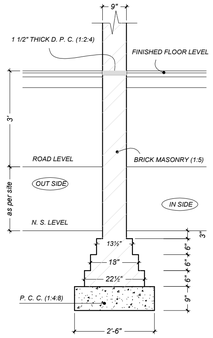

KEY PLAN
SCALE (1" = 32'-0")



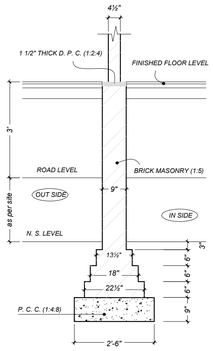

SITE PLAN
SCALE (1" = 16')



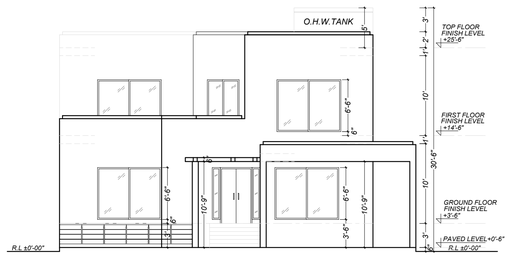

9" TH. EXTERNAL WALL
footing detail
SCALE :- (1" = 2')



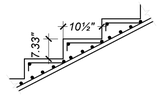

9" TH. INTERNAL WALL
footing detail
SCALE :- (1" = 2')



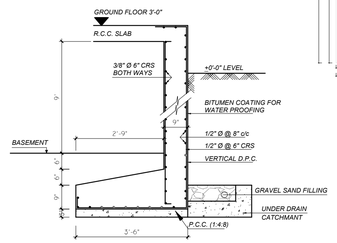

4½"TH.INTERNALWALL
footing detail
SCALE :- (1" = 2')



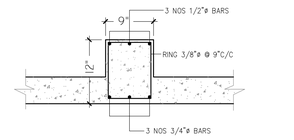

FRONT ELEVATION
SCALE (1" = 8'-0")



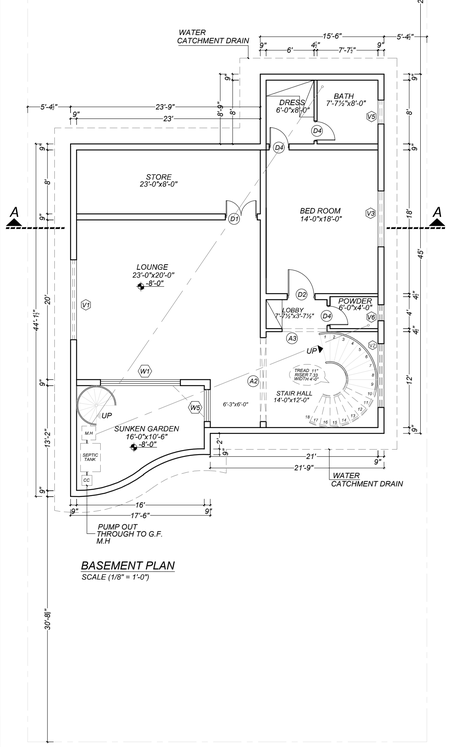

STAIR STEPS DETAIL
SCALE : 1"=2'-0"



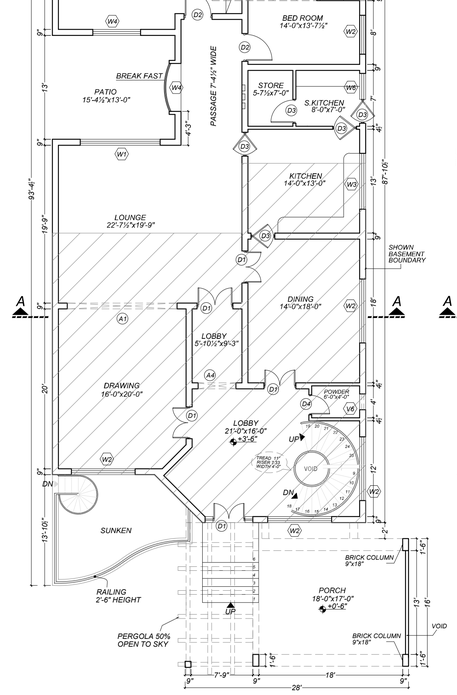

RETAINING WALL
SCALE 1" = 2'-0"



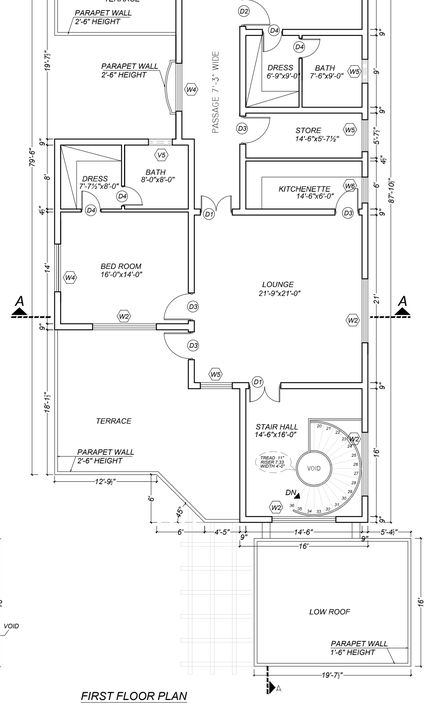

BEAM DEATIL
SCALE; 1"=1'-0"



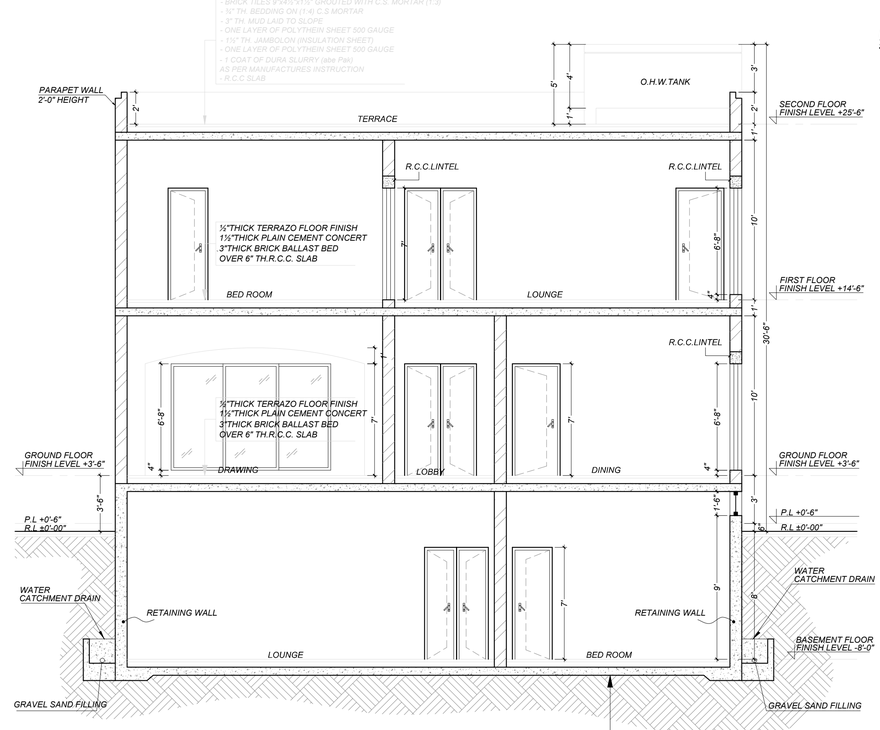

BASEMENT PLAN
SCALE (1/8" = 1'-0")




GROUND FLOOR PLAN
SCALE (1/8" = 1'-0")




FIRST FLOOR PLAN
SCALE (1/8" = 1'-0")




SECTION A-A
SCALE (1" = 4')

NORTH

SCHEDULE OF DOORS, WINDOWS AND VENTILATORS

DOORS:

| TYPE | SIZE | CILL | STYLE | DESCRIPTION |
|---|---|---|---|---|
| D1 | 4'-0"x7'-0" | 0'-0" | DOUBLE SHUTTER | WOODEN GLASS DOOR |
| D2 | 3'-6"x7'-0" | 0'-0" | SINGLE SHUTTER | 〃 〃 〃 |
| D3 | 3'-0"x7'-0" | 0'-0" | 〃 | 〃 〃 〃 |
| D4 | 2'-6"x7'-0" | 0'-0" | 〃 | 〃 |

WINDOWS:

| TYPE | SIZE | CILL | STYLE | DESCRIPTION |
|---|---|---|---|---|
| W1 | 10'-0"x6'-8" | 0'-6" | STRAIGHT | ALUMINIUM WITH GLASS |
| W2 | 8'-0"x6'-8" | 0'-6" | 〃 | 〃 〃 〃 |
| W3 | 7'-0"x3'-6" | 3'-6" | 〃 | 〃 〃 〃 |
| W4 | 6'-0"x6'-8" | 0'-6" | 〃 | 〃 〃 〃 |
| W5 | 4'-0"x6'-8" | 0'-6" | 〃 | 〃 〃 〃 |
| W6 | 3'-3"x3'-6" | 3'-6" | 〃 | 〃 〃 〃 |

VENTILATOR

| TYPE | SIZE | CILL | STYLE | DESCRIPTION |
|---|---|---|---|---|
| V1 | 10'-0"x1'-6" | 8'-6" | STRAIGHT | ALUMINIUM WITH GLASS |
| V2 | 8'-0"x1'-6" | 8'-6" | 〃 | 〃 〃 〃 |
| V3 | 7'-0"x1'-6" | 8'-6" | 〃 | 〃 〃 〃 |
| V4 | 6'-0"x1'-6" | 8'-6" | 〃 | 〃 〃 〃 |
| V5 | 3'-0"x1'-6" | 8'-6" | 〃 | 〃 〃 〃 |
| V6 | 2'-0"x1'-6" | 8'-6" | 〃 | 〃 〃 〃 |

ARCHES:

| TYPE | SIZE | CILL | STYLE |
|---|---|---|---|
| A1 | 13'-9"x7'-0" | 0'-0" | SEGMENTED |
| A2 | 10'-6"x7'-0" | 0'-0" | 〃 〃 |
| A3 | 6'-0"x7'-0" | 0'-0" | FLAT |
| A4 | 4'-4½"x7'-0" | 0'-0" | SEGMENTED |

SCHEDULE OF AREA

| | | |
|---|---|---|
| 1. | TOTAL PLOT AREA | = 6,590/- Sft |
| 2. | COV. AREA OF BASEMENT | = 1,874/- Sft |
| 3. | COV. AREA OF G.F. | = 3,438/- Sft |
| 4. | COV. AREA OF F.F. | = 2,599/- Sft |
| 5. | TOTAL COVERED AREA | = 7,911/- Sft |
| 6. | OPEN AREA | = 3,152/- Sft |

SCHEDULE OF BARS BANDING

| RMNO | M.BARS | D.BARS |
|---|---|---|
| RM-1 | #4@5" | #4@7" |
| RM-2 | #3@5" | #3@7" |
| RM-3 | #3@4" | #3@6" |
| RM-4 | #3@6" | #3@6" |
| RM-5 | #3@7" | #3@9" |

- BRICK TILES 9"x4½"x1½" GROUTED WITH C.S. MORTAR (1:3)
- ½" TH. BEDDING ON (1:4) C.S MORTAR
- 3" TH. MUD LAID TO SLOPE
- ONE LAYER OF POLYTHEIN SHEET 500 GAUGE
- 1½" TH. JAMBOLON (INSULATION SHEET)
- ONE LAYER OF POLYTHEIN SHEET 500 GAUGE
- 1 COAT OF DURA SLURRY (abe Pak)
AS PER MANUFACTURES INSTRUCTION
- R.C.C SLAB

DRAWING NO.

JOB TITLE

PROPOSED HOUSE DESIGN FOR Mrs.AYESHA MAHMOOD PLOT NO 446 SECTOR -H DEFENCE HOUSING PHASE V AUTHORITY. LAHORE LAHORE CANTT

SUB JOB TITLE

SUBMISSION DRAWING

DRG.TITLE

PLAN'S ELEVATION SECTION & DETAIL

ARCHITECT: NAYYAR ALI DADA

DRAWN BY: MARYAM ISLAM

CHECKED BY: HASSAN

SCALE: AS SHOWN

OWNER SIG.

NAYYAR ALI DADA & ASSOCIATES
6F/3 NEW MUSLIM TOWN,LAHORE.
Phones 5864884-5864191.