

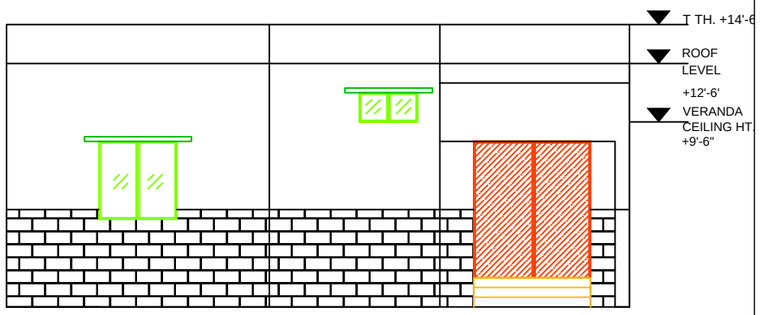



## ELEVATION
SCALE:1/8"=1'

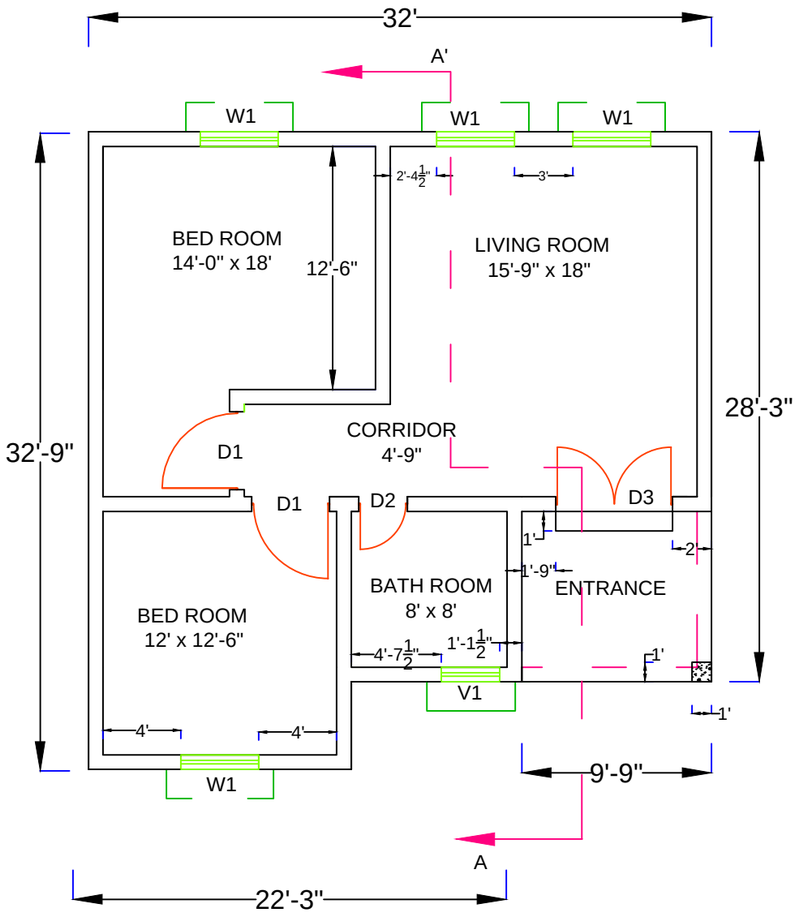


## PLAN
SCALE:1/8"=1'

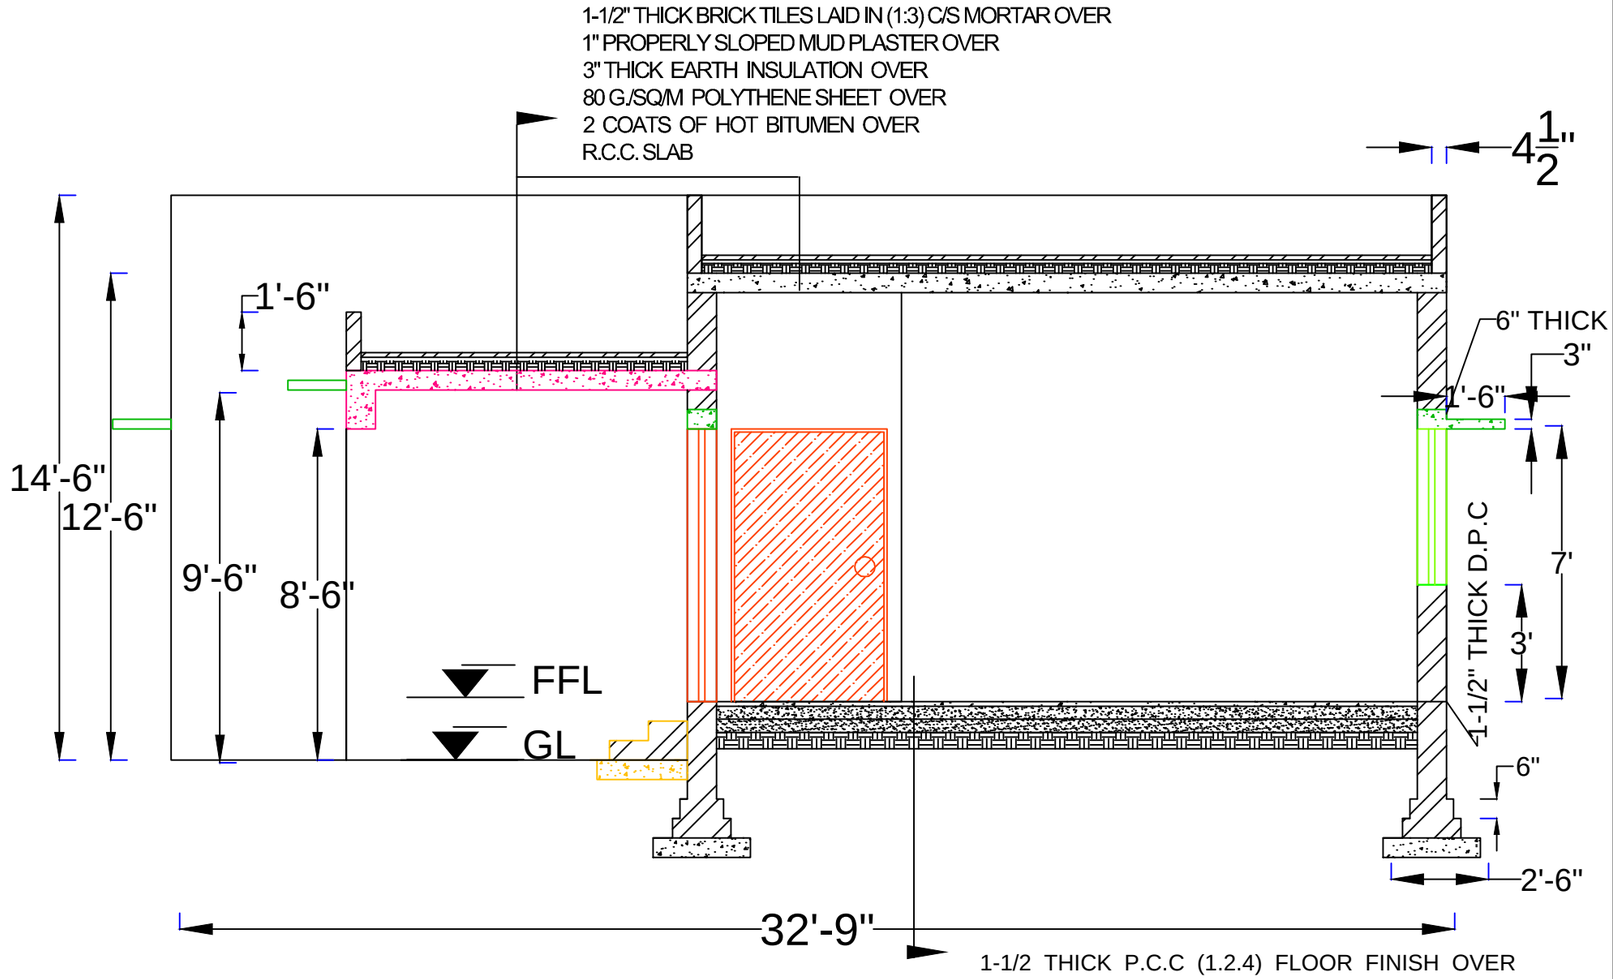


## SECTION A-A
SCALE:1/4"=1'0"

1-1/2 THICK P.C.C (1.2.4) FLOOR FINISH OVER
4" THICK P.C.C (1:4:8) OVER
4" THICK SAND CUSHION OVER
WELL COMPACTED EARTH

### SCHEDULE OF VALUES

| SR# | ITEM | SILL LEVEL(W.R.T.P.L) | QUANTITY | DESCRIPTION |
|---|---|---|---|---|
| 1 | D1 | 4'-0"X7'-0" | 0'-0" | WOODEN PANELLED SINGLE LEAF DOOR |
| 2 | D2 | 2'-6"X7"-0" | 0'-0" | WOODEN PANELLED SINGLE LEAF DOOR |
| 3 | D3 | 6'-0"X7'-0' | 0'-0" | WOODEN PANELLED SIGNLE LEAF DOOR |
| 4 | W1 | 4'-0"X4'-0' | +3'-0' | STEEL PANELLED GLAZED WINDOW WITH WIRE GAUZE |
| 5 | V1 | 3'-0"X1'-6" | 8'-0" | STEEL PANELLED GLAZED VENTILATOR WITH WIRE GAUZE |

### TITLE BOX

| | |
|---|---|
| NUST | SCEE,NICE |
| 2019 | SECTION A |
| PROJECT | BUILDING DRAWING |
| DRAWN BY | RIDA NOOR INTIKHAB 173279 |
| SCALE | MENTIONED |
| DATE | 2/19/2019 |